Развертка кухни

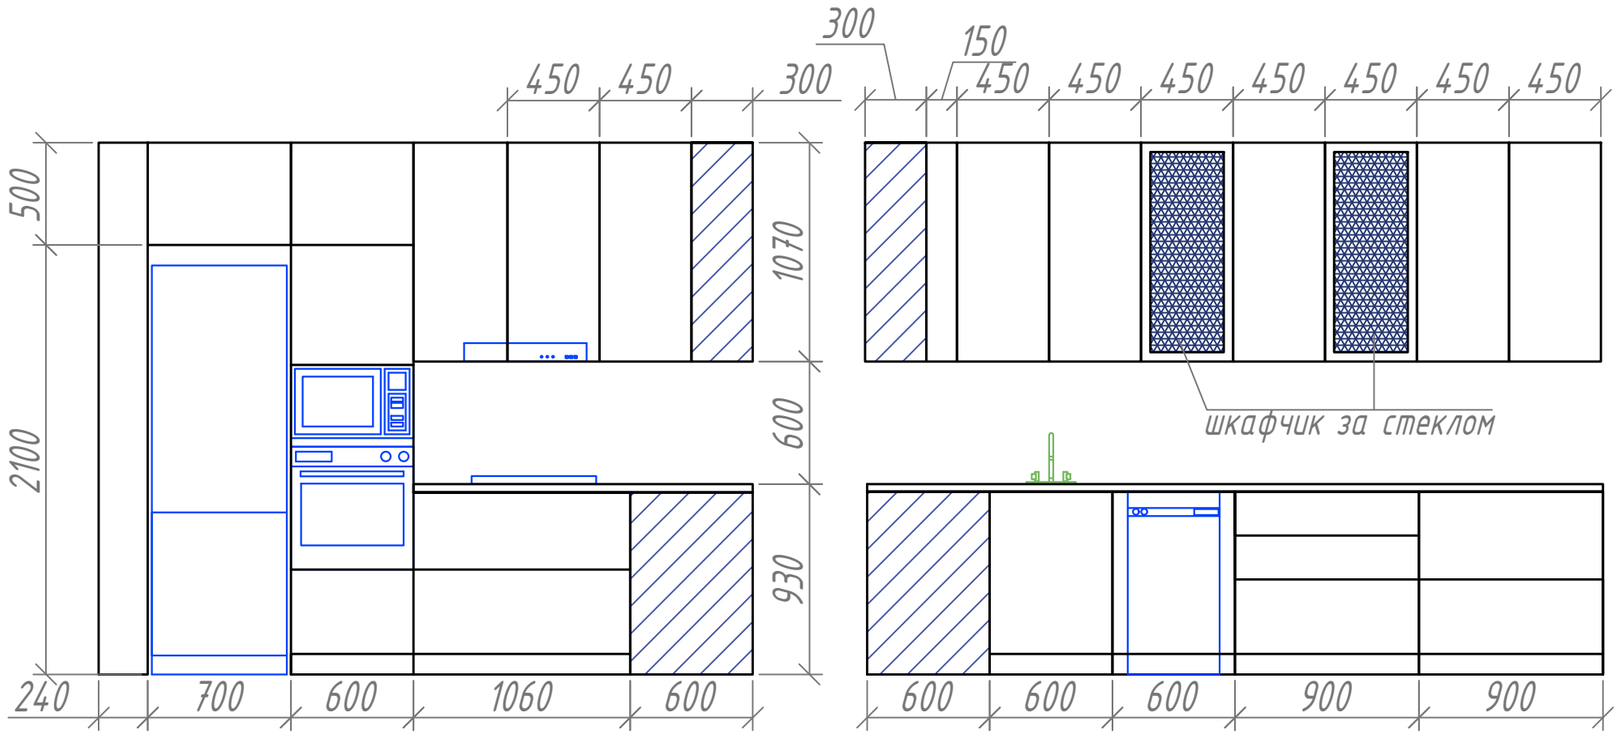

Примечание :

- *Точные размеры смотреть по месту*
- *Рекомендации по возведению конструкций уточнять у специалиста*
- *Высоту ниши для холодильника отрегулировать после покупки холодильника*
- *Посудомоечная машина 450 мм.*
- *Ручки гола профиль*

Дизайнер	Абрамчук Юлия		ЖК "Минск-Мир" дом "Танго"	Стадия	Лист	Листов
	Кривицкая Светлана			ДП	12	
Заказчики	Сергей		Развертка кухни 1:30	Дизайнеры интерьера Кривицкая светлана (29)304-59-32 Абрамчук Юлия (44)795-87-47		
	Марина					